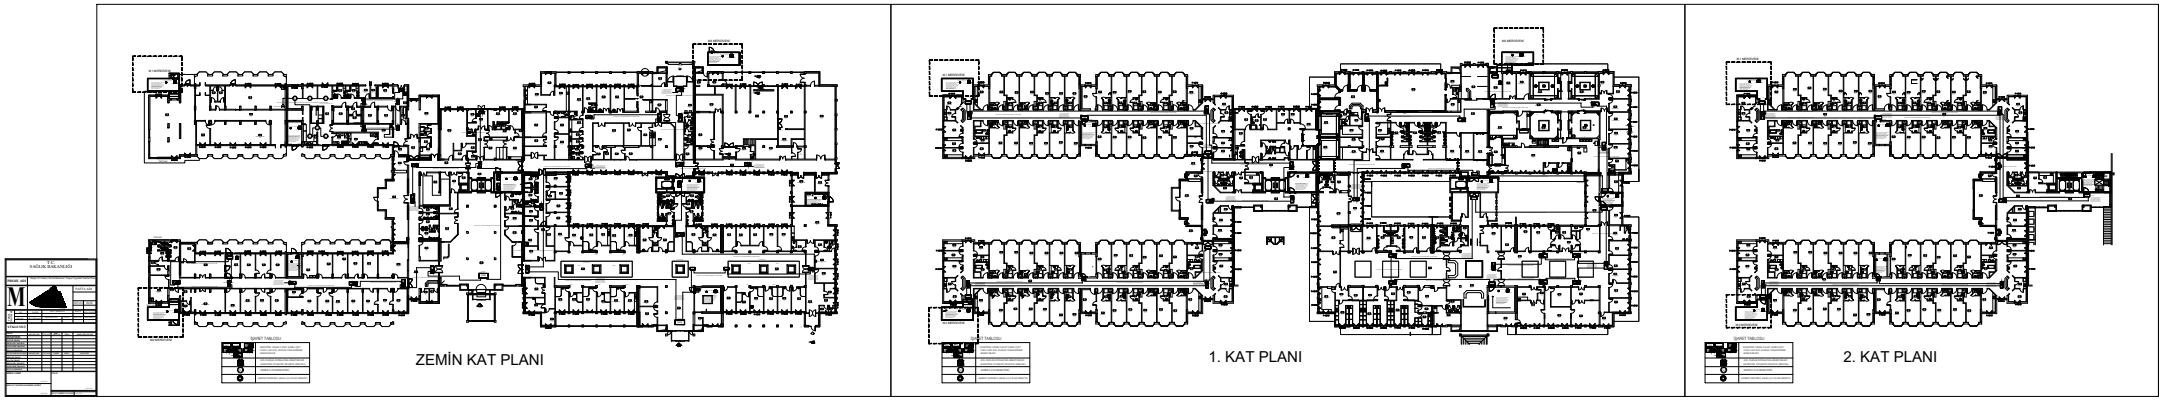

FETHİYE DEVLET HASTANESİ YANGIN ALGILAMA-ACİL DURUM YÖNLENDİRME PROJESİ

ELEKTRİK PROJESİNE AİT GENEL NOTLAR

1. ELEKTRİK PROJESİ GERİNİMİ 380/220V 50Hz 3-F 4-DİL(MALZEMELERİN YÜKLENİŞİ 4 YİVİNİ ZORLAYACAK)
2. PROJE SUPERVİZÖRÜ, ÖRNEĞİN TİPİ DETAYLARI PROJESİ İÇİN ÖNCEDEN ONAYLATILMALIDIR.
3. PROJE SUPERVİZÖRÜ, ÖRNEĞİN TİPİ DETAYLARI PROJESİ İÇİN ÖNCEDEN ONAYLATILMALIDIR. UYGULAMA SÜRASINDA, MALZEQ İYİ PİYASADA DETAYLARI ESASTIR
4. ONAYLANDIKTAN SONRA UYGULAMAYA GEÇİLEBİLİR.
5. ÖNCEDEN ONAYLANMAMIŞ MALZEME VE UYGULAMA ONAYLANMAMIŞTIR. ONAYSIZ TİPİ İÇİN ÇALIŞAN KİŞİNİN İŞİNİ ALMAK YÖNÜNDEN SORUMLU LUĞUNDADIR.
6. BİNLERİN HALLERİNİN NANEO PARALARINA BİNLERİNİZİN KONULMASI İÇİN TİPİ İÇİN İLİT HASTANESİ TİPİNİN KİMİNDEN ALINCAKTIR.
7. YENİNİNİNİNİ MAHALNİDİR BİLİNMİ İÇİN OLİ DİSİDİR TİPİNİNİN BİLİNİ İÇİ VAKLYA İRTİBATLANDIRILARAK ÇALIŞIR DURUMA GETİRİLMİŞİ İMİŞLANCAKTIR.
8. YAPILAN TÜM BİNLİ İLİM TİPİ İÇİN İÇİN İLİT HASTANESİ İLİMİNİNİ TİPİNİN İÇİLİNİ İÇİLİCİKTİR.